




Plan coffrage Fondation

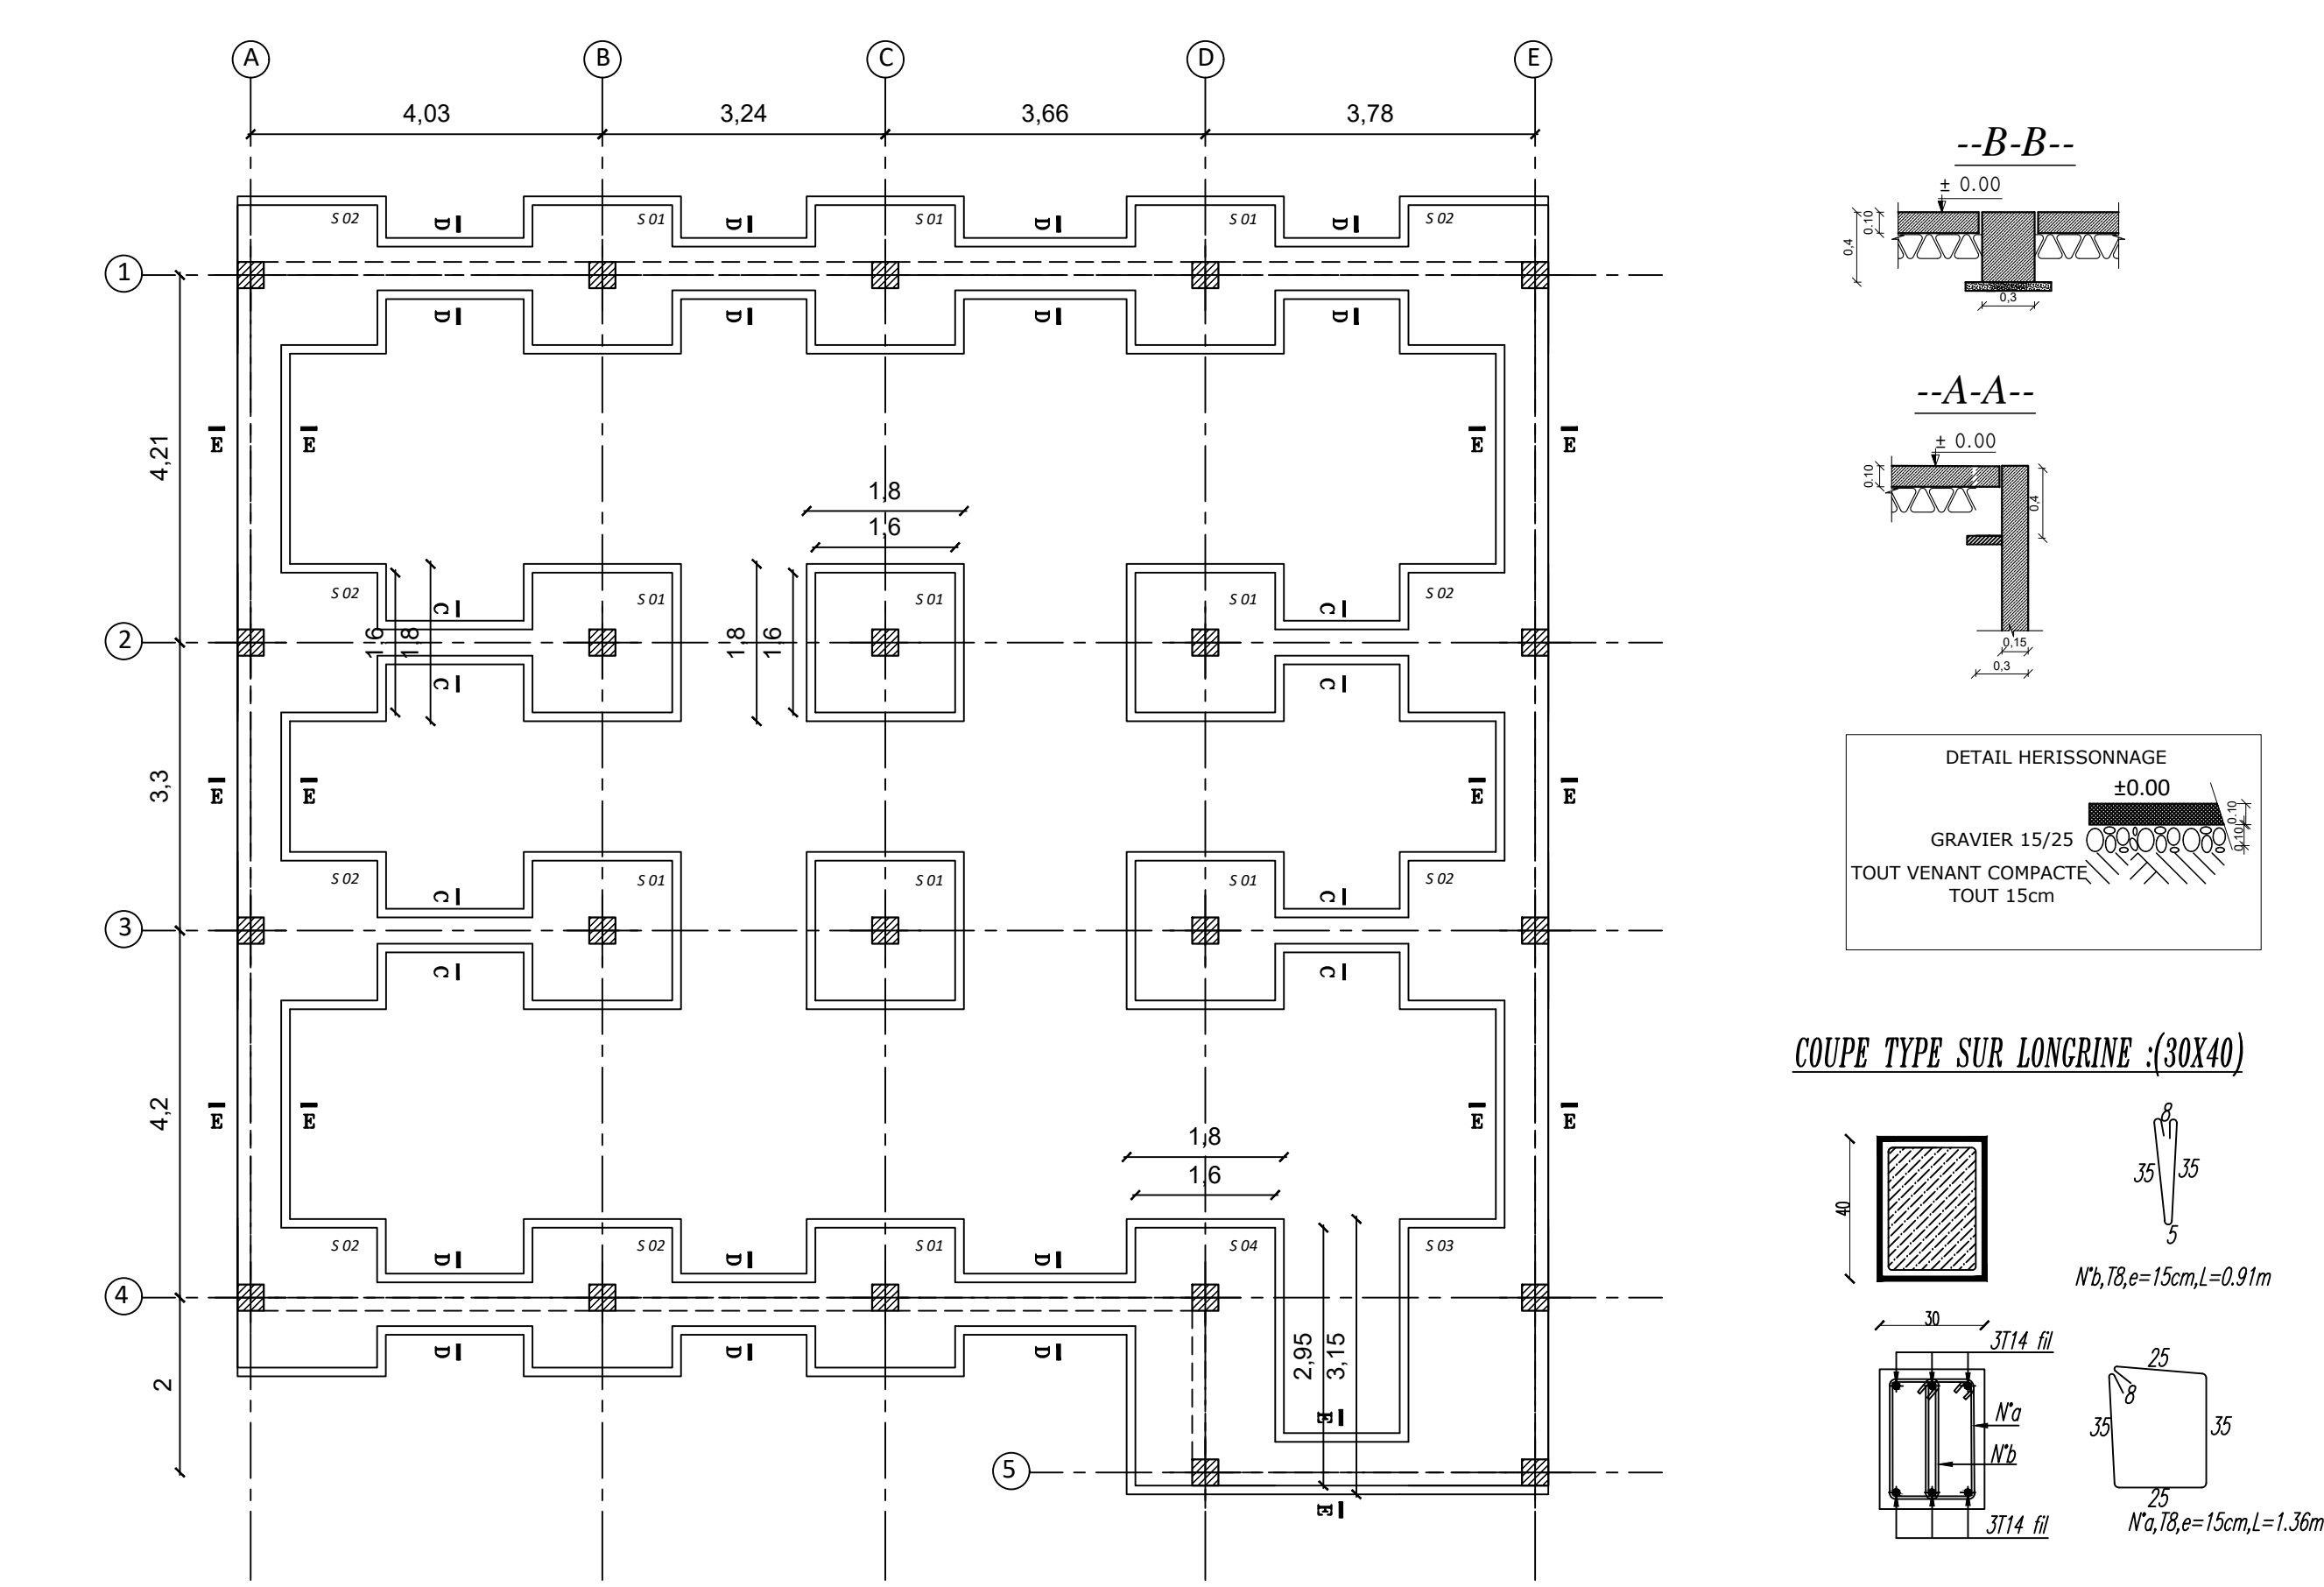



Plan coffrage Niv RDC

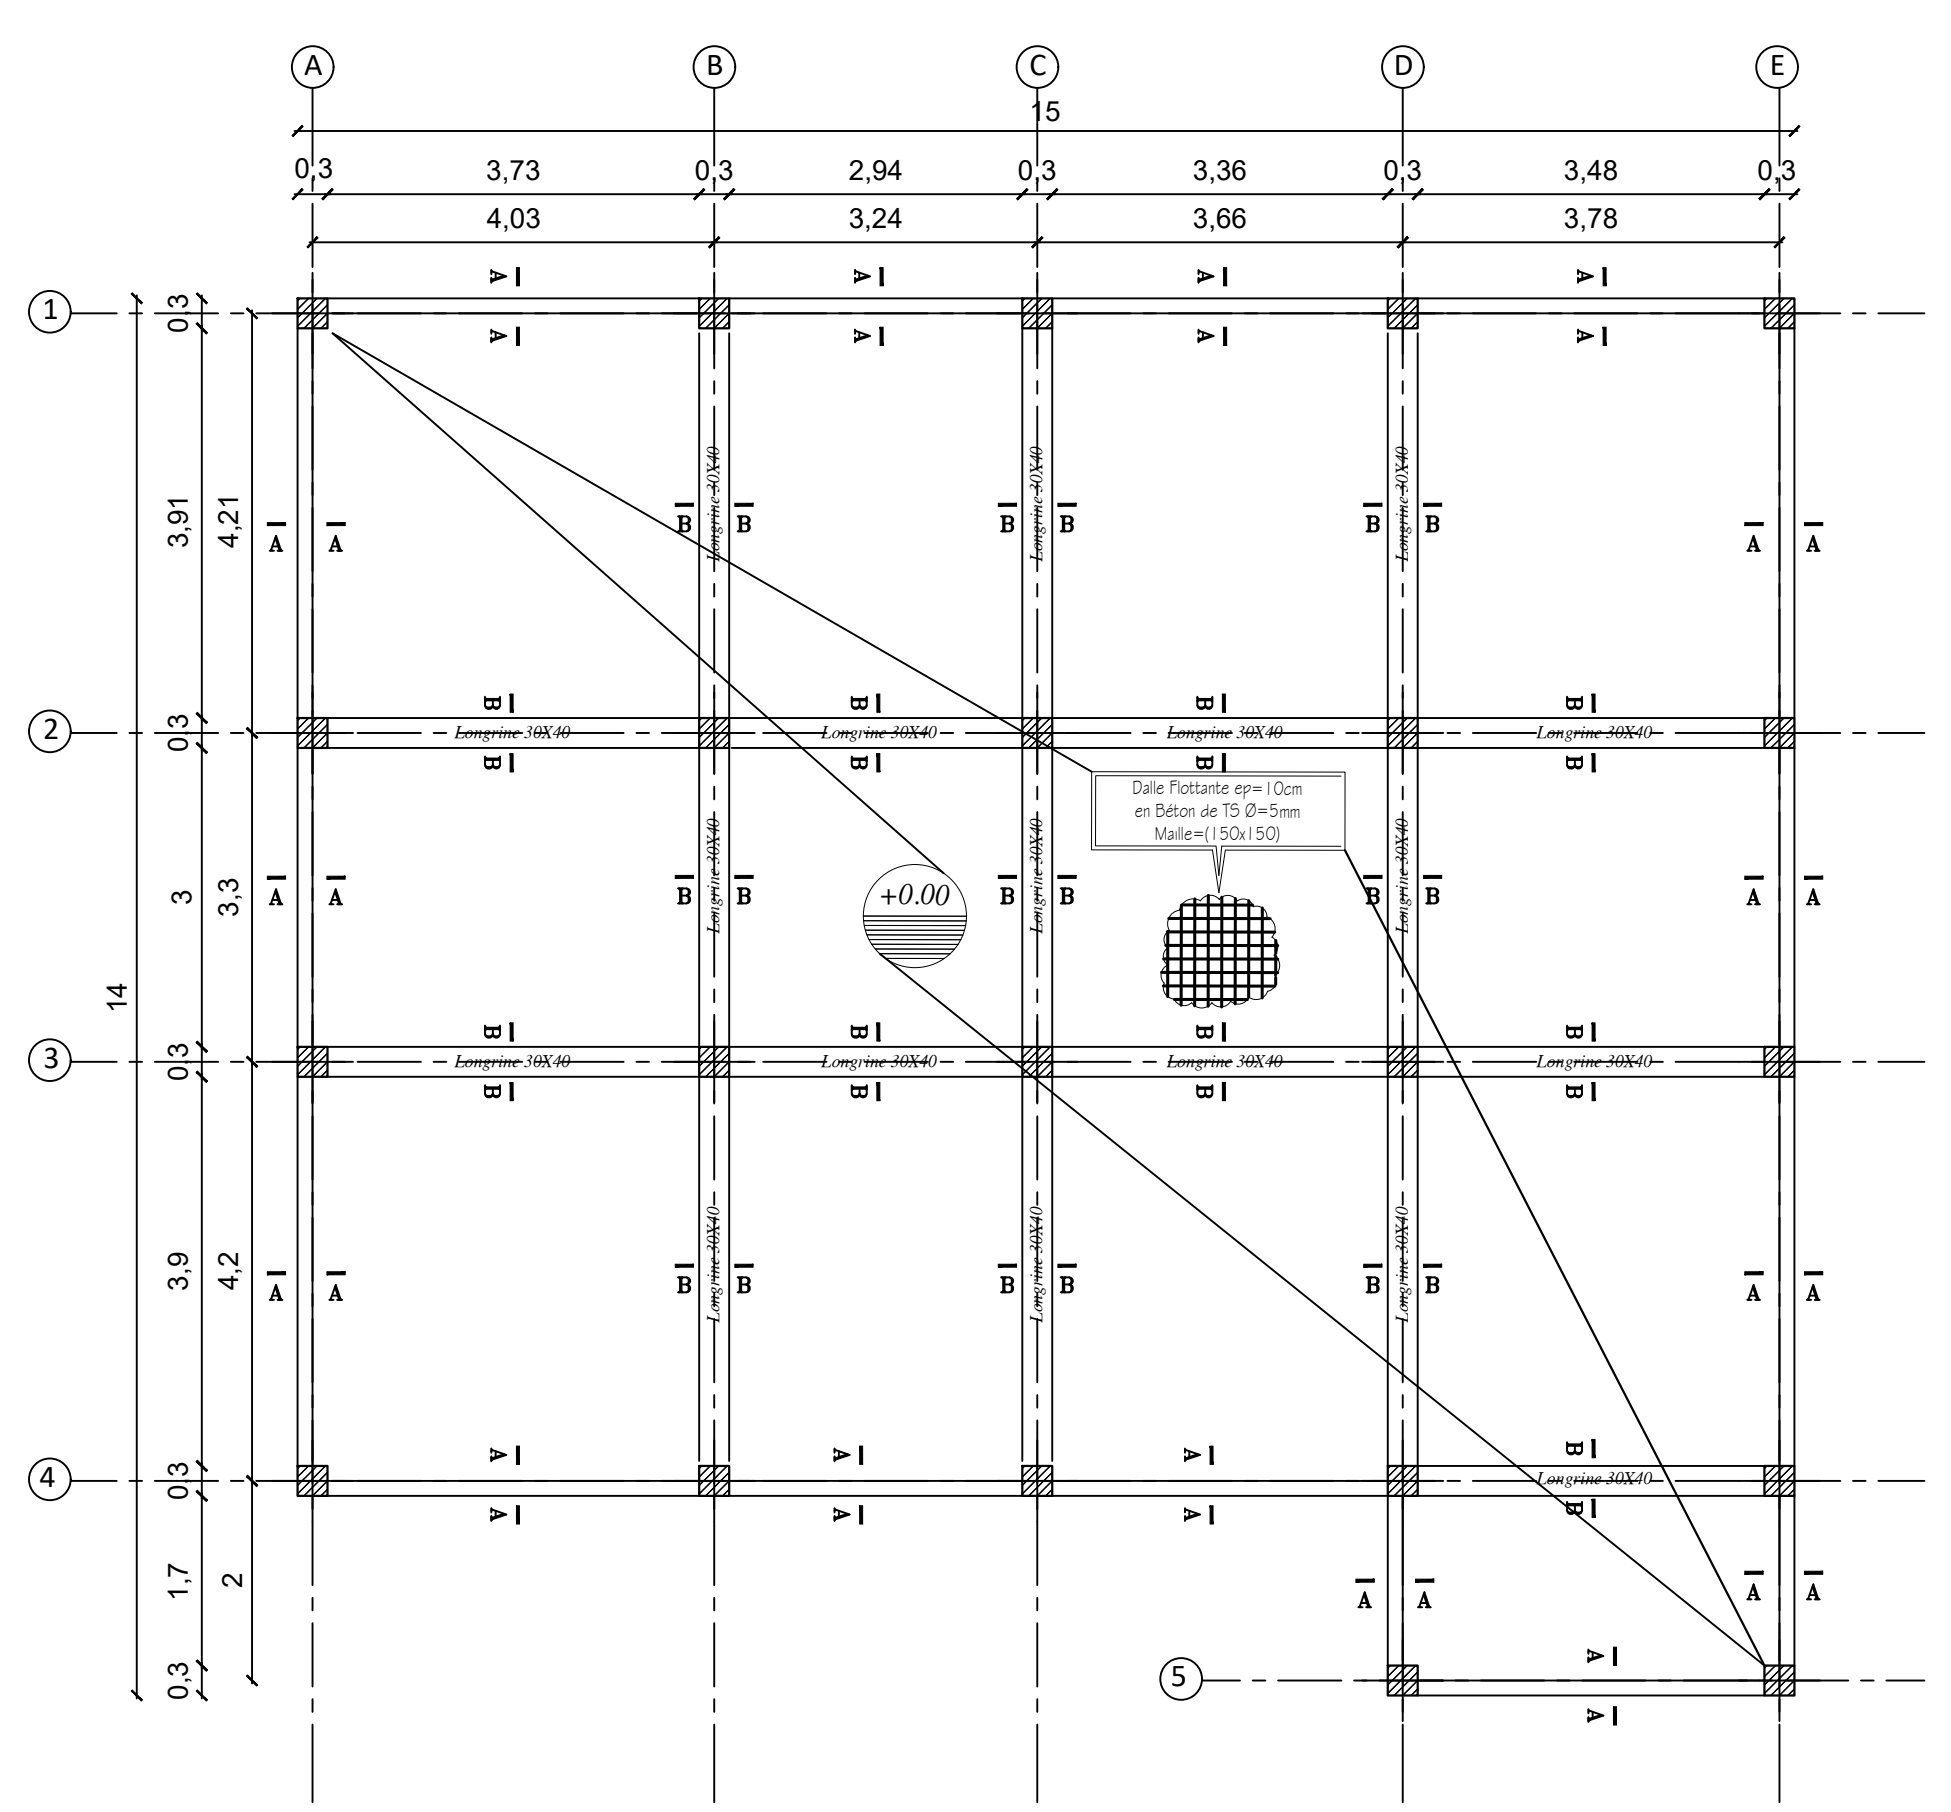


Plan coffrage Niv +3.57

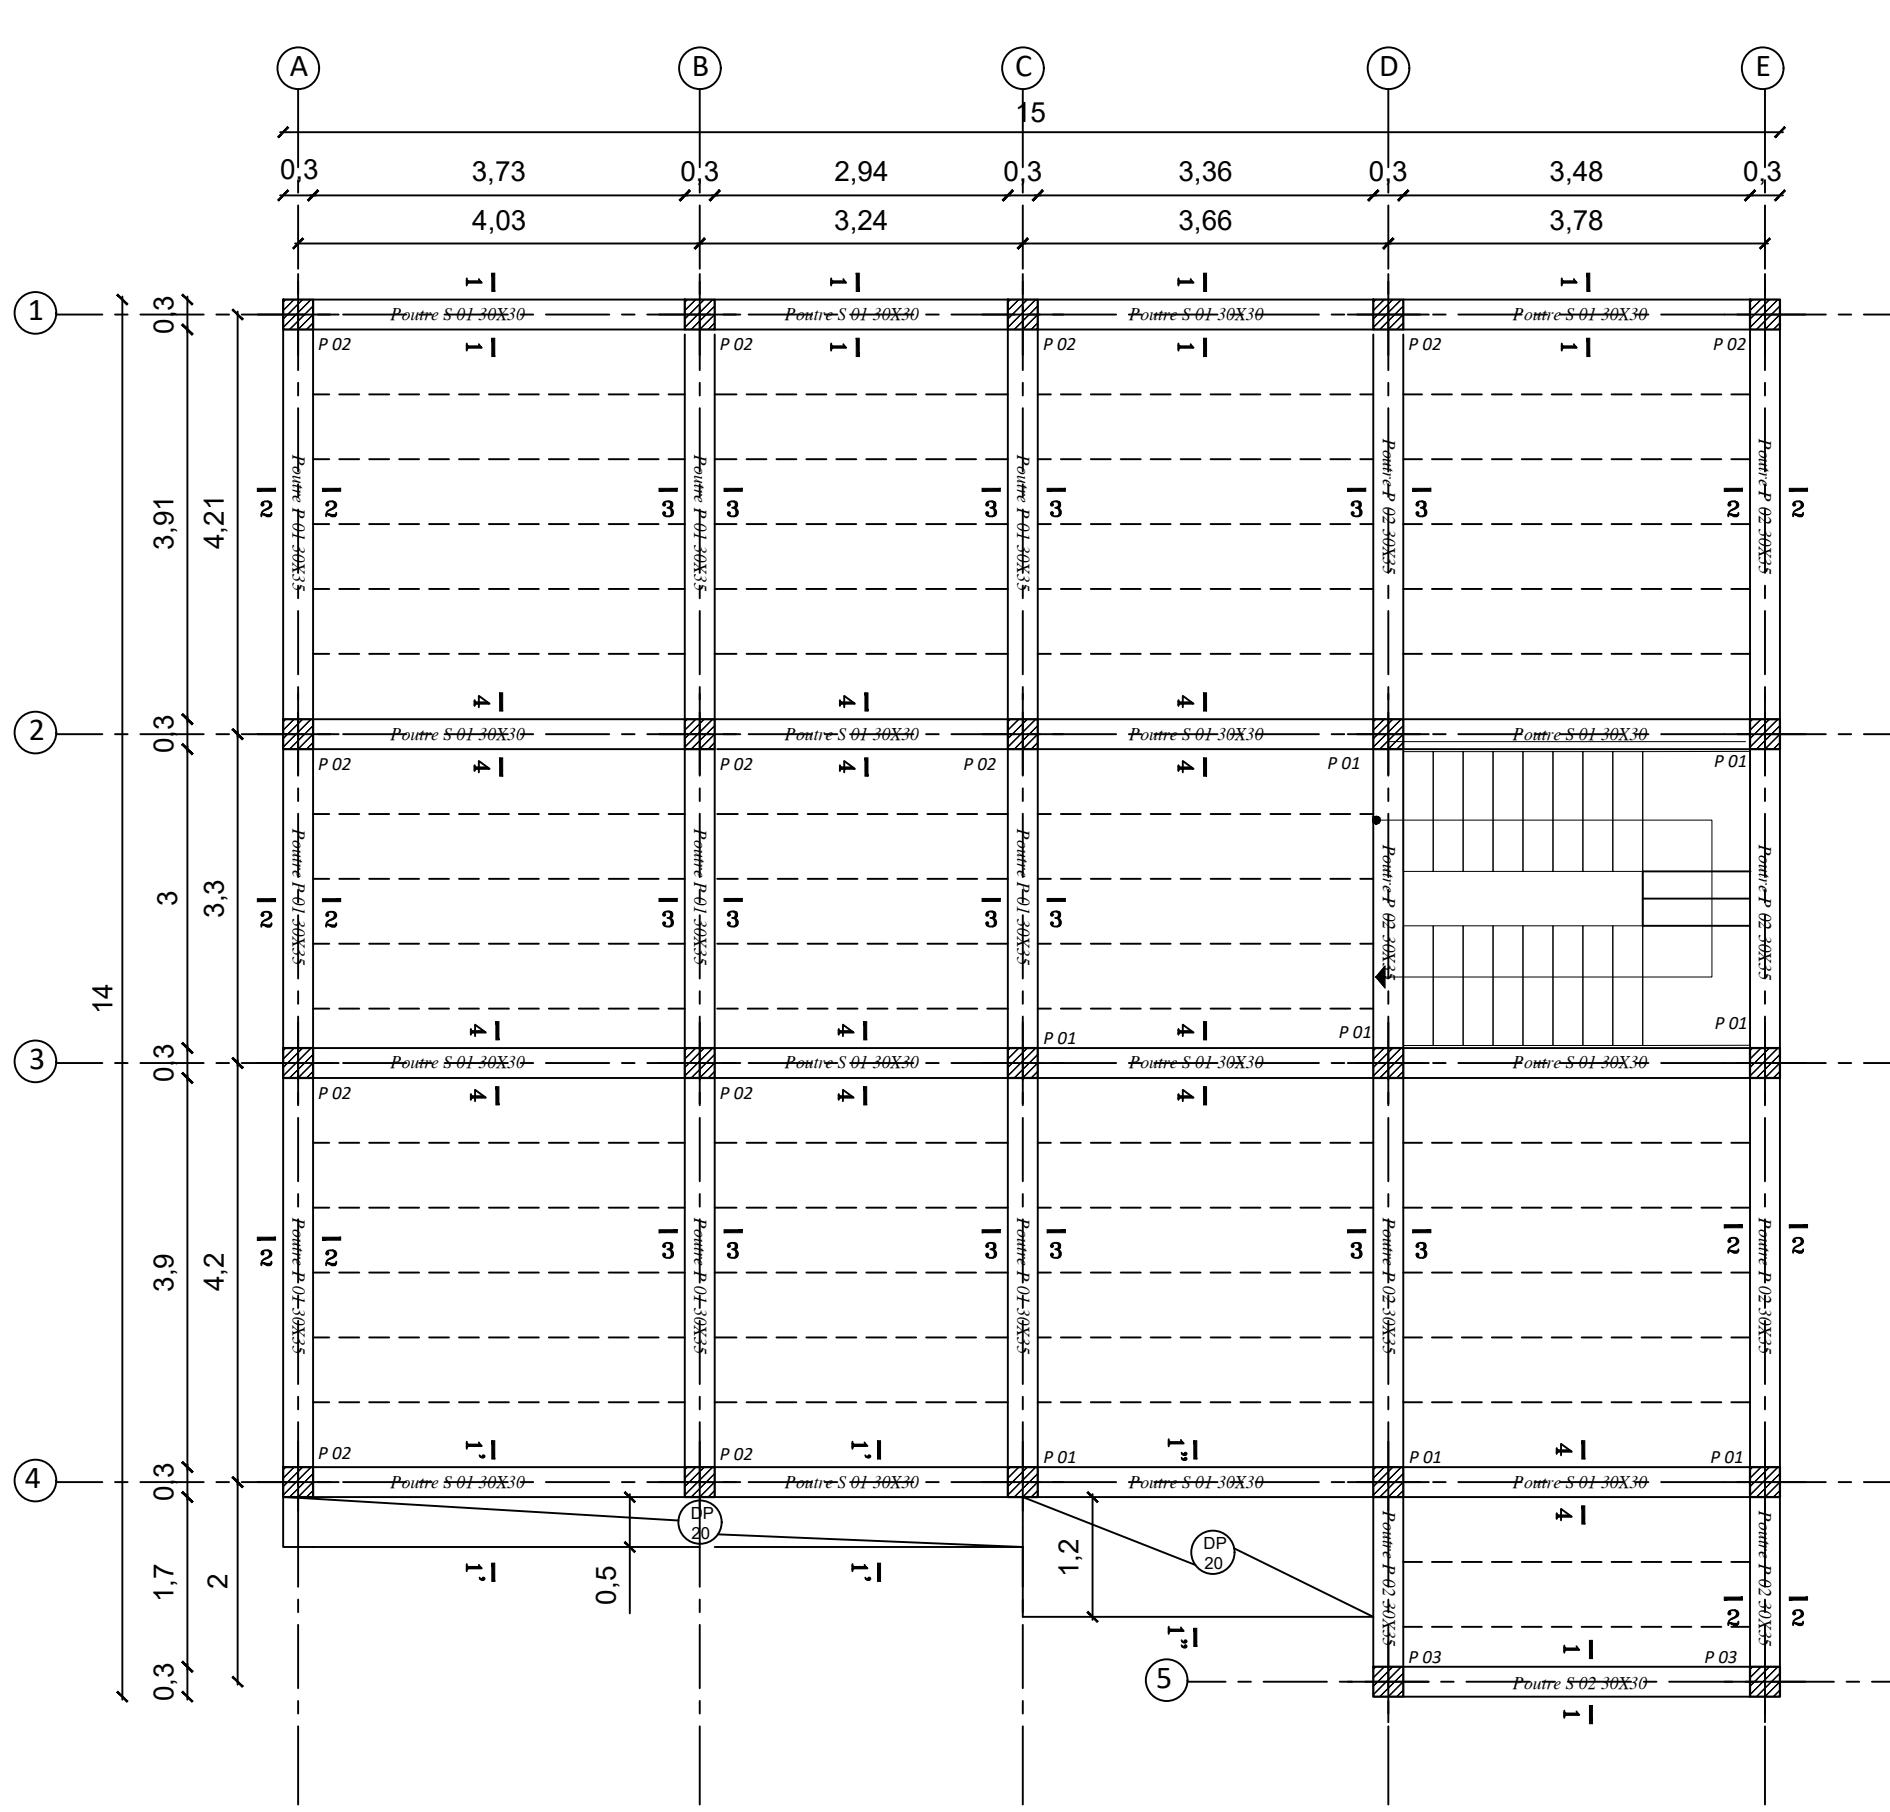


Plan coffrage Niv +6.63

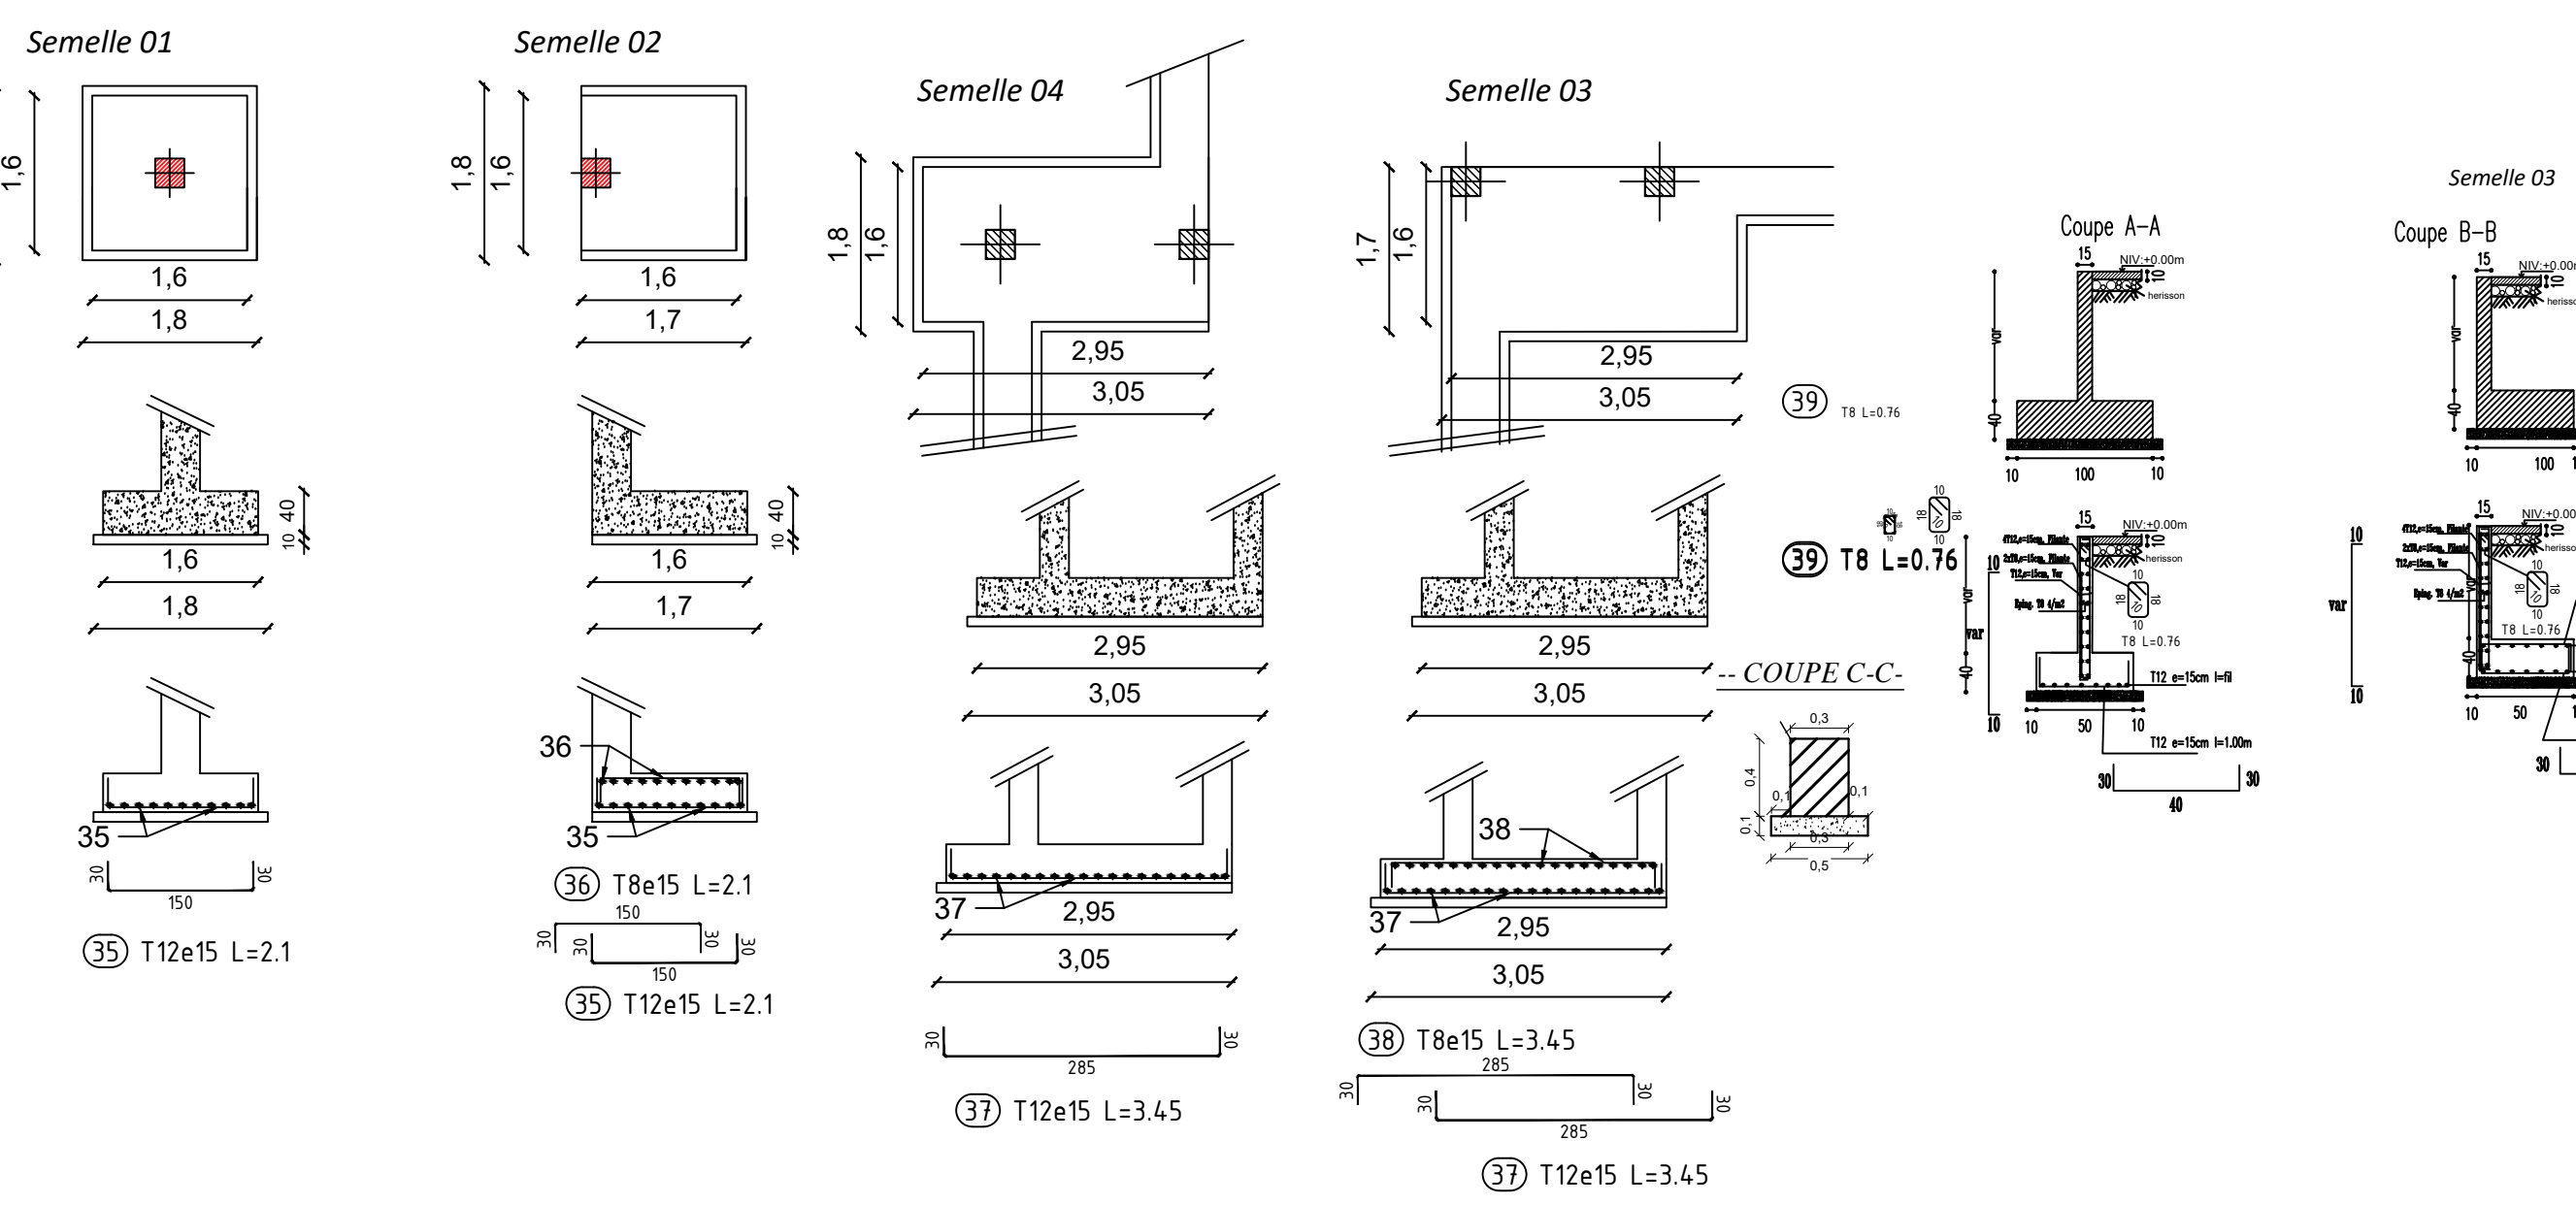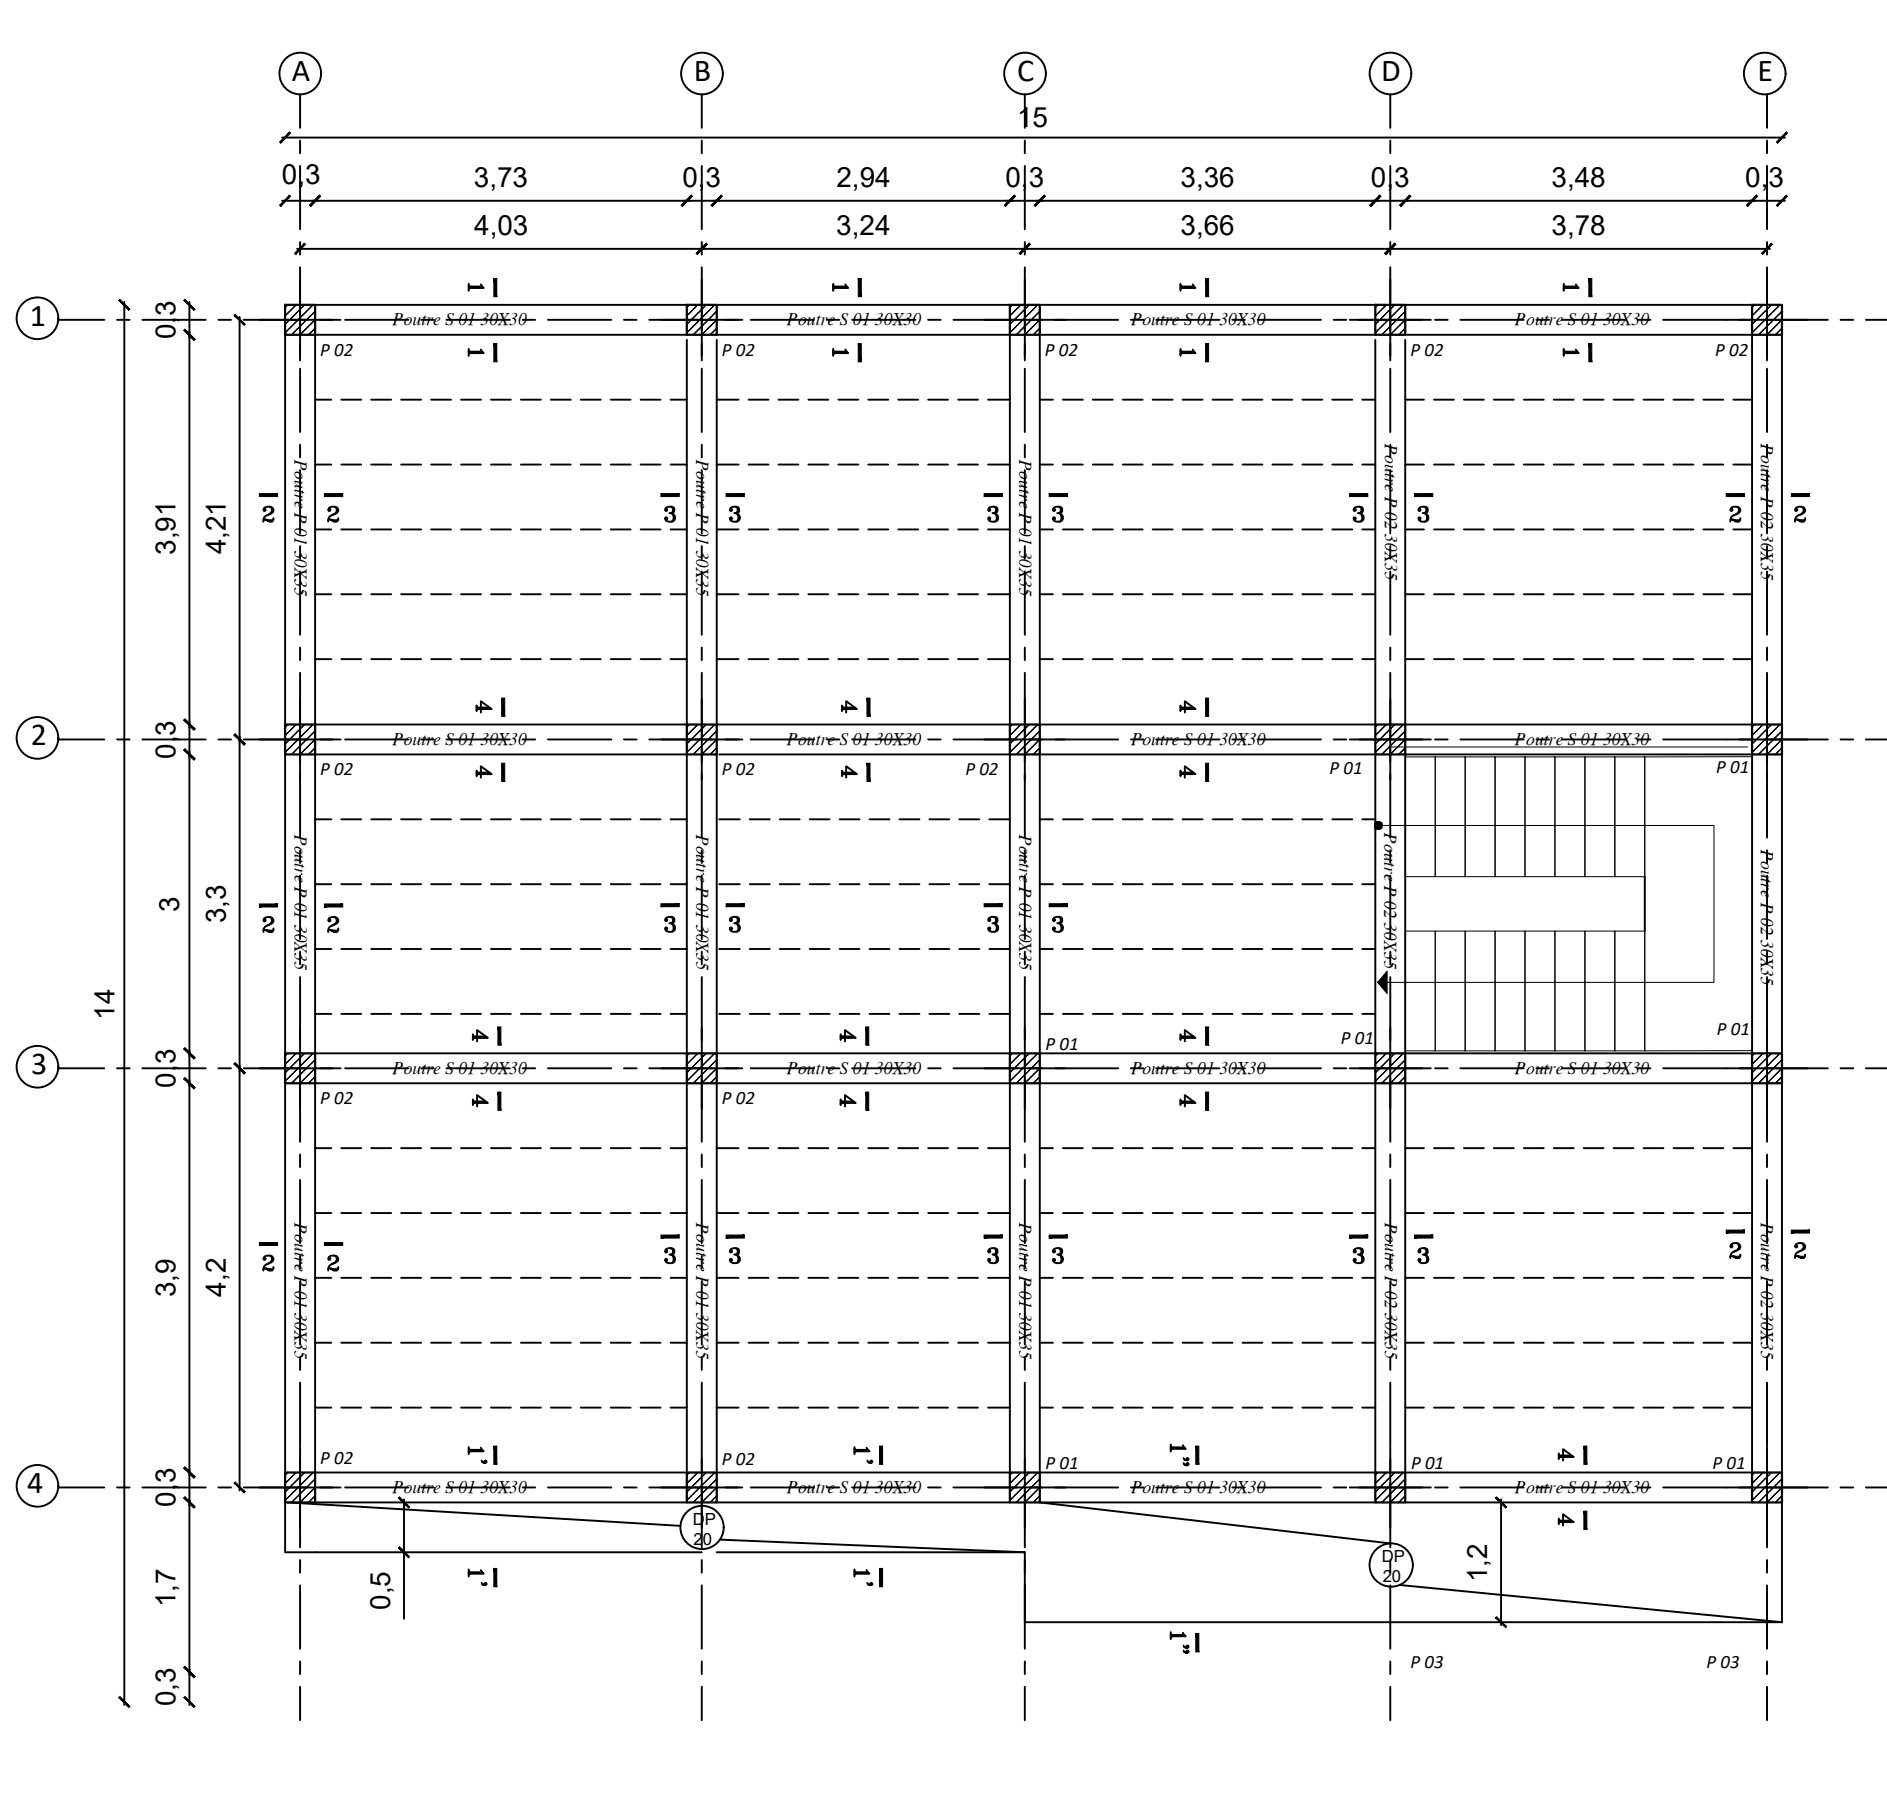





Coffrage Ferrailage Poutres

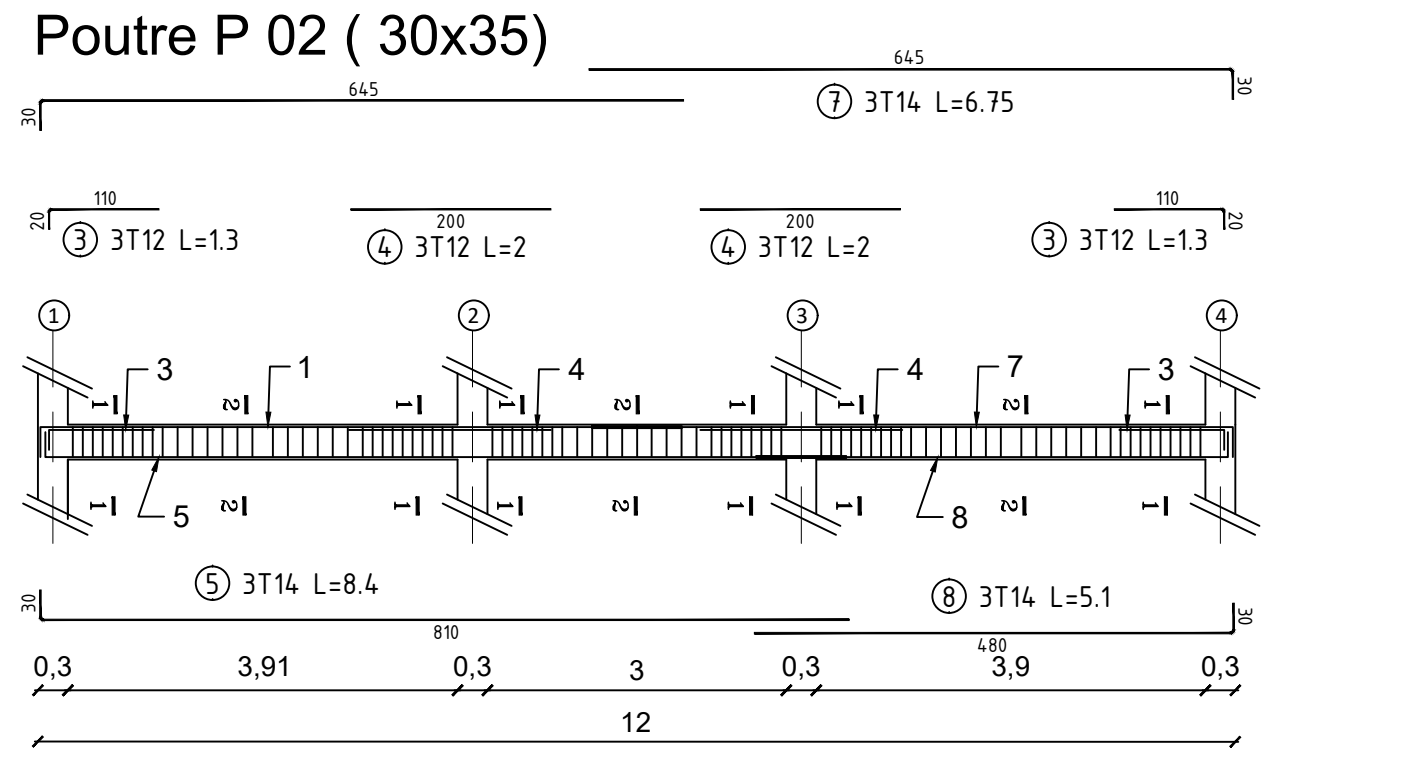


Plan coffrage Niv +9.69

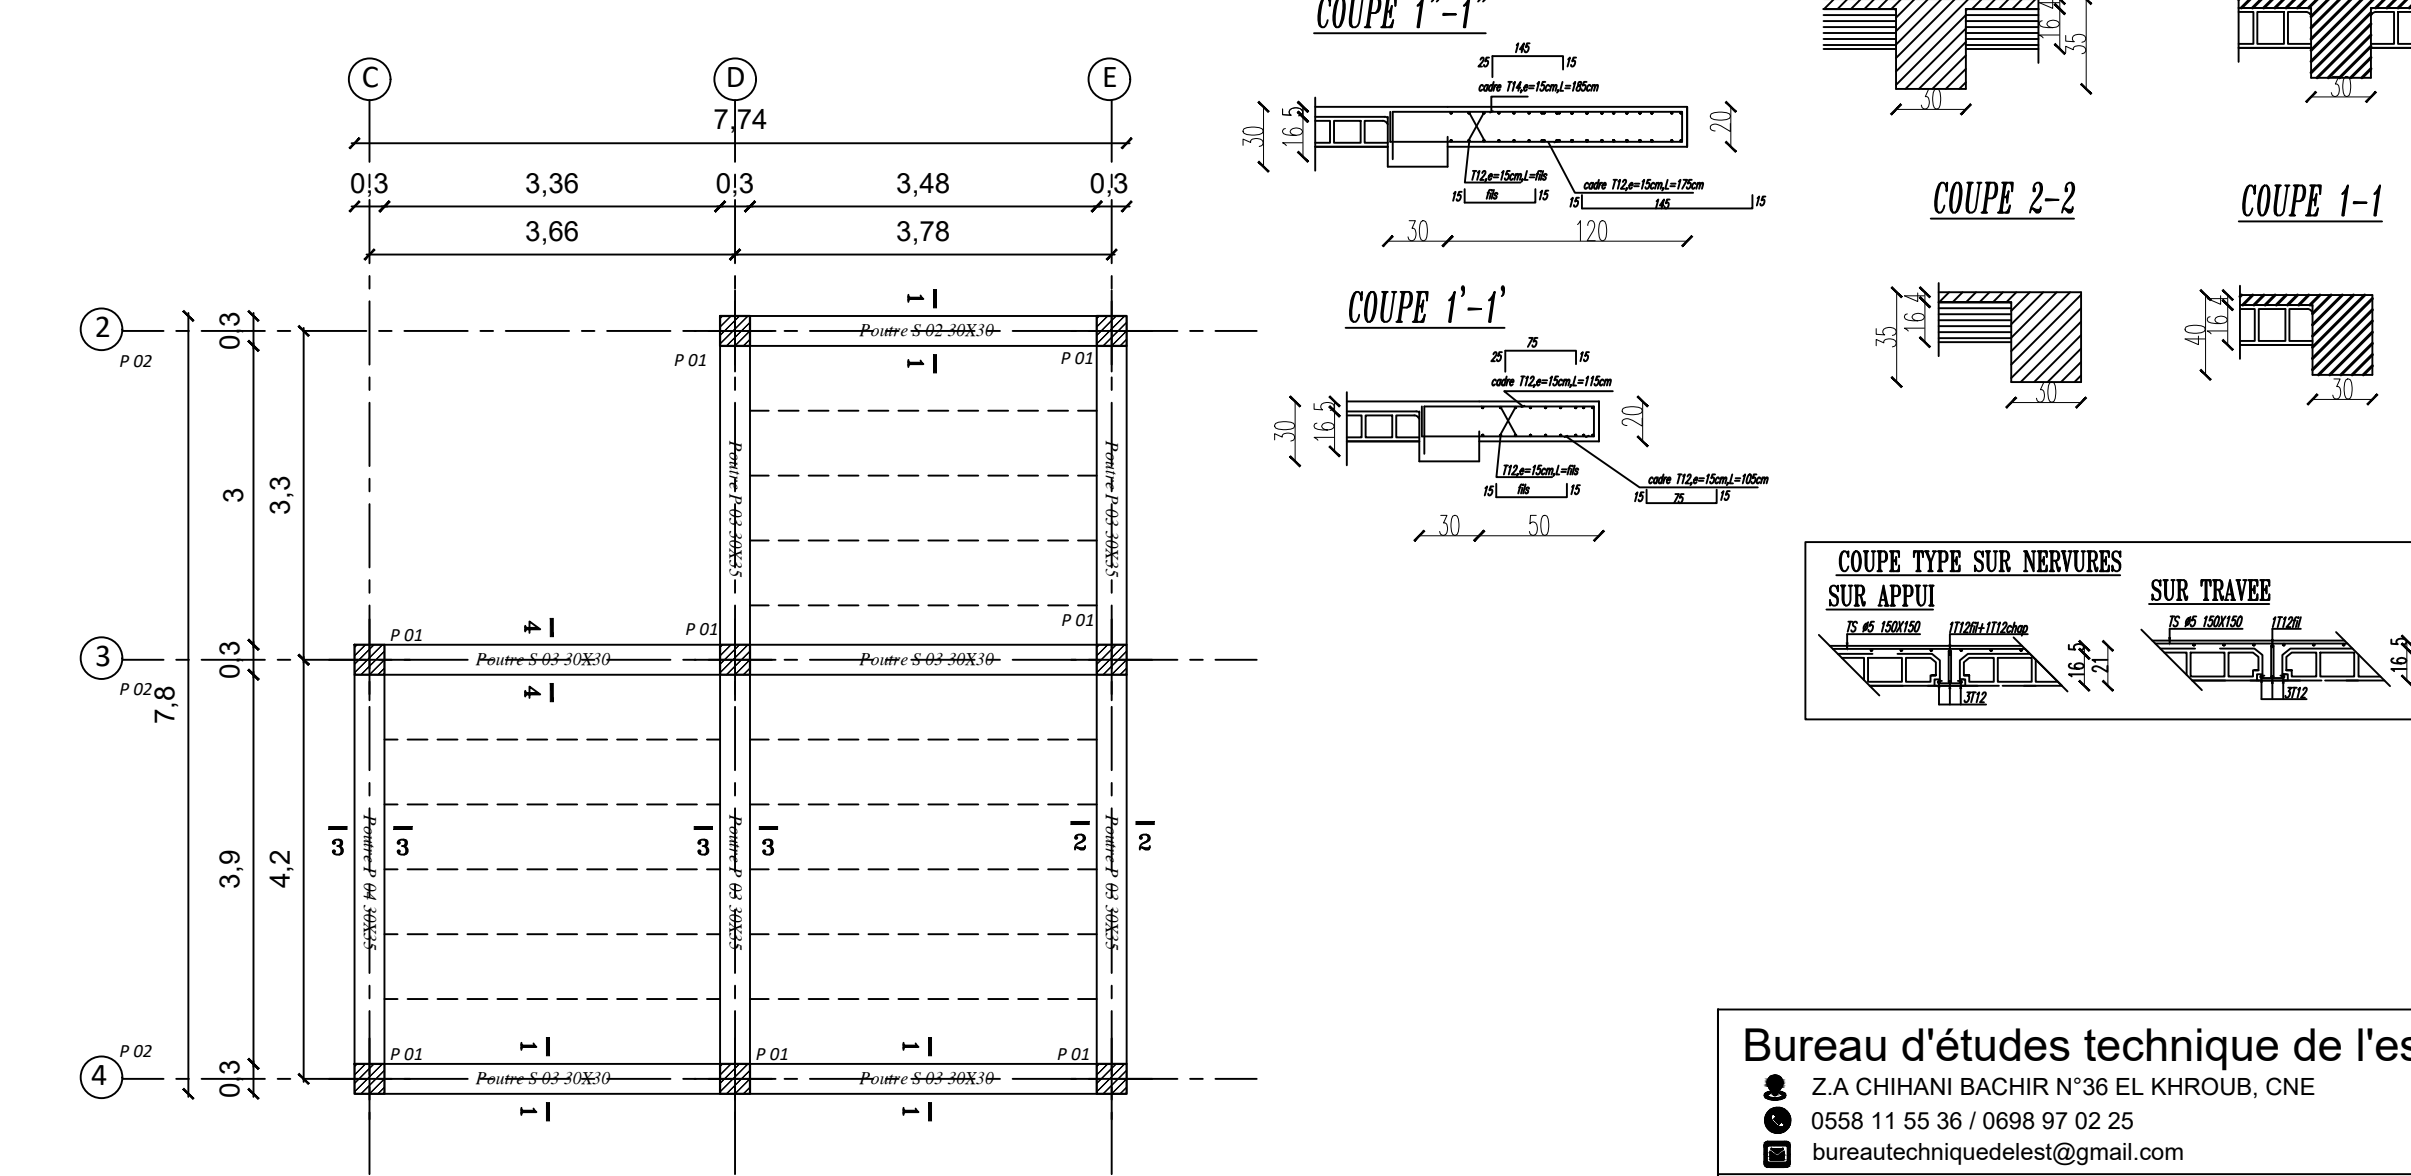

Coffrage Ferrailage Poteaux

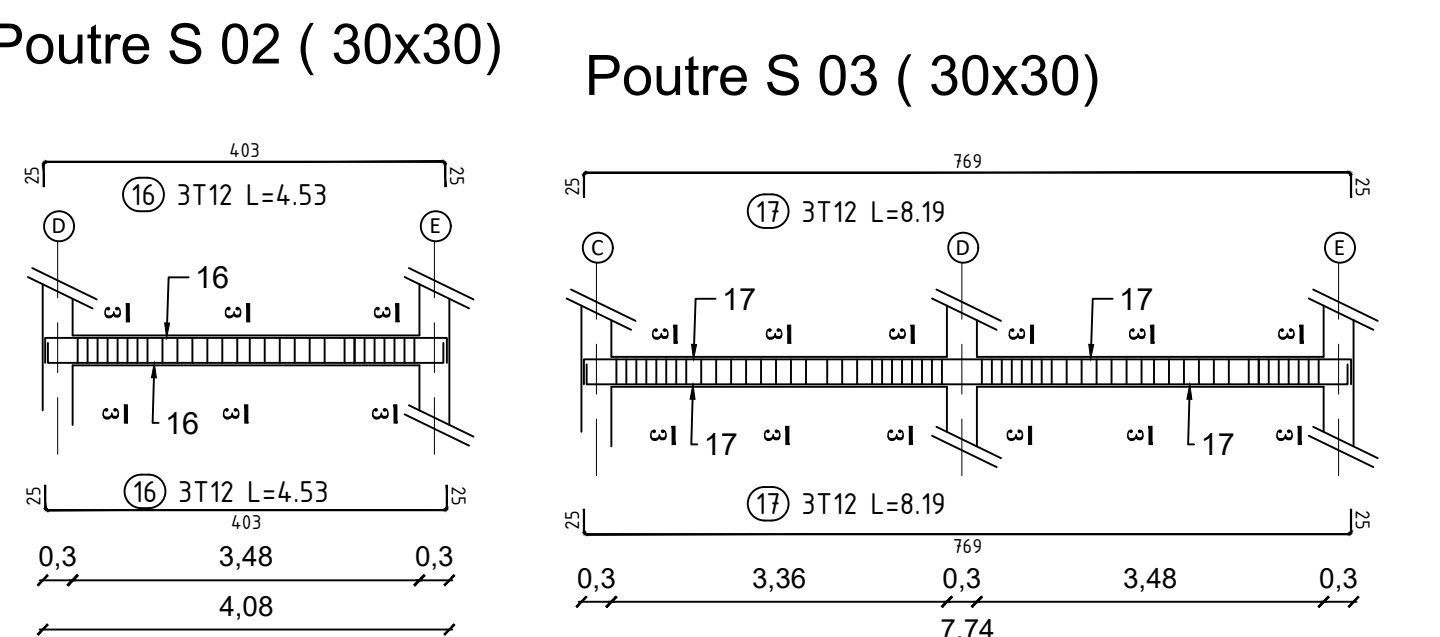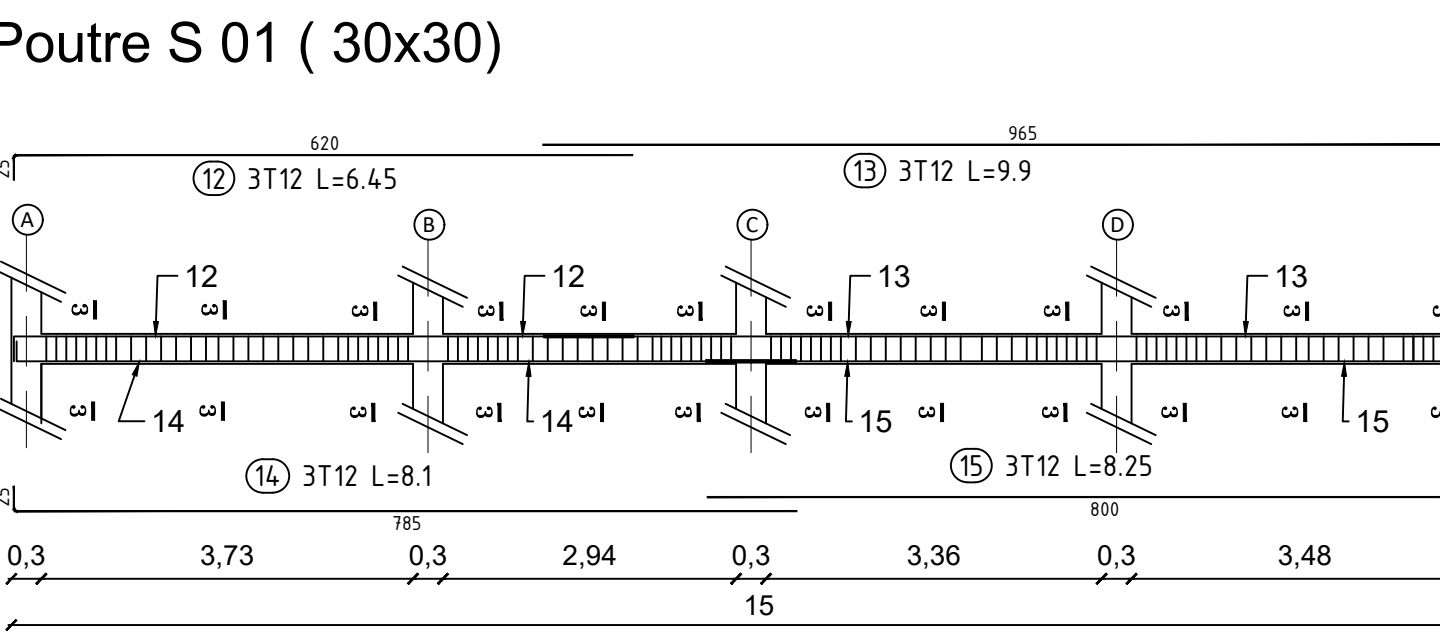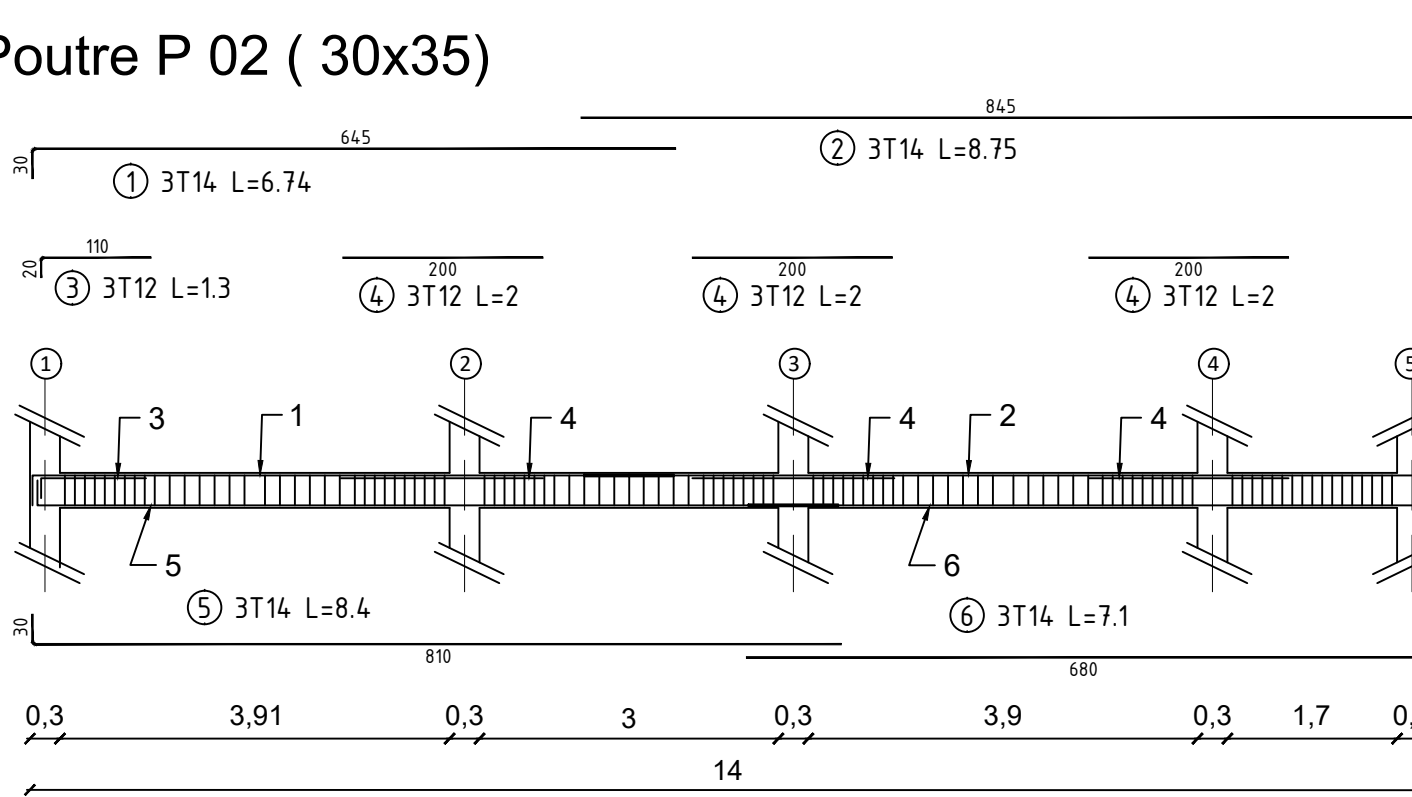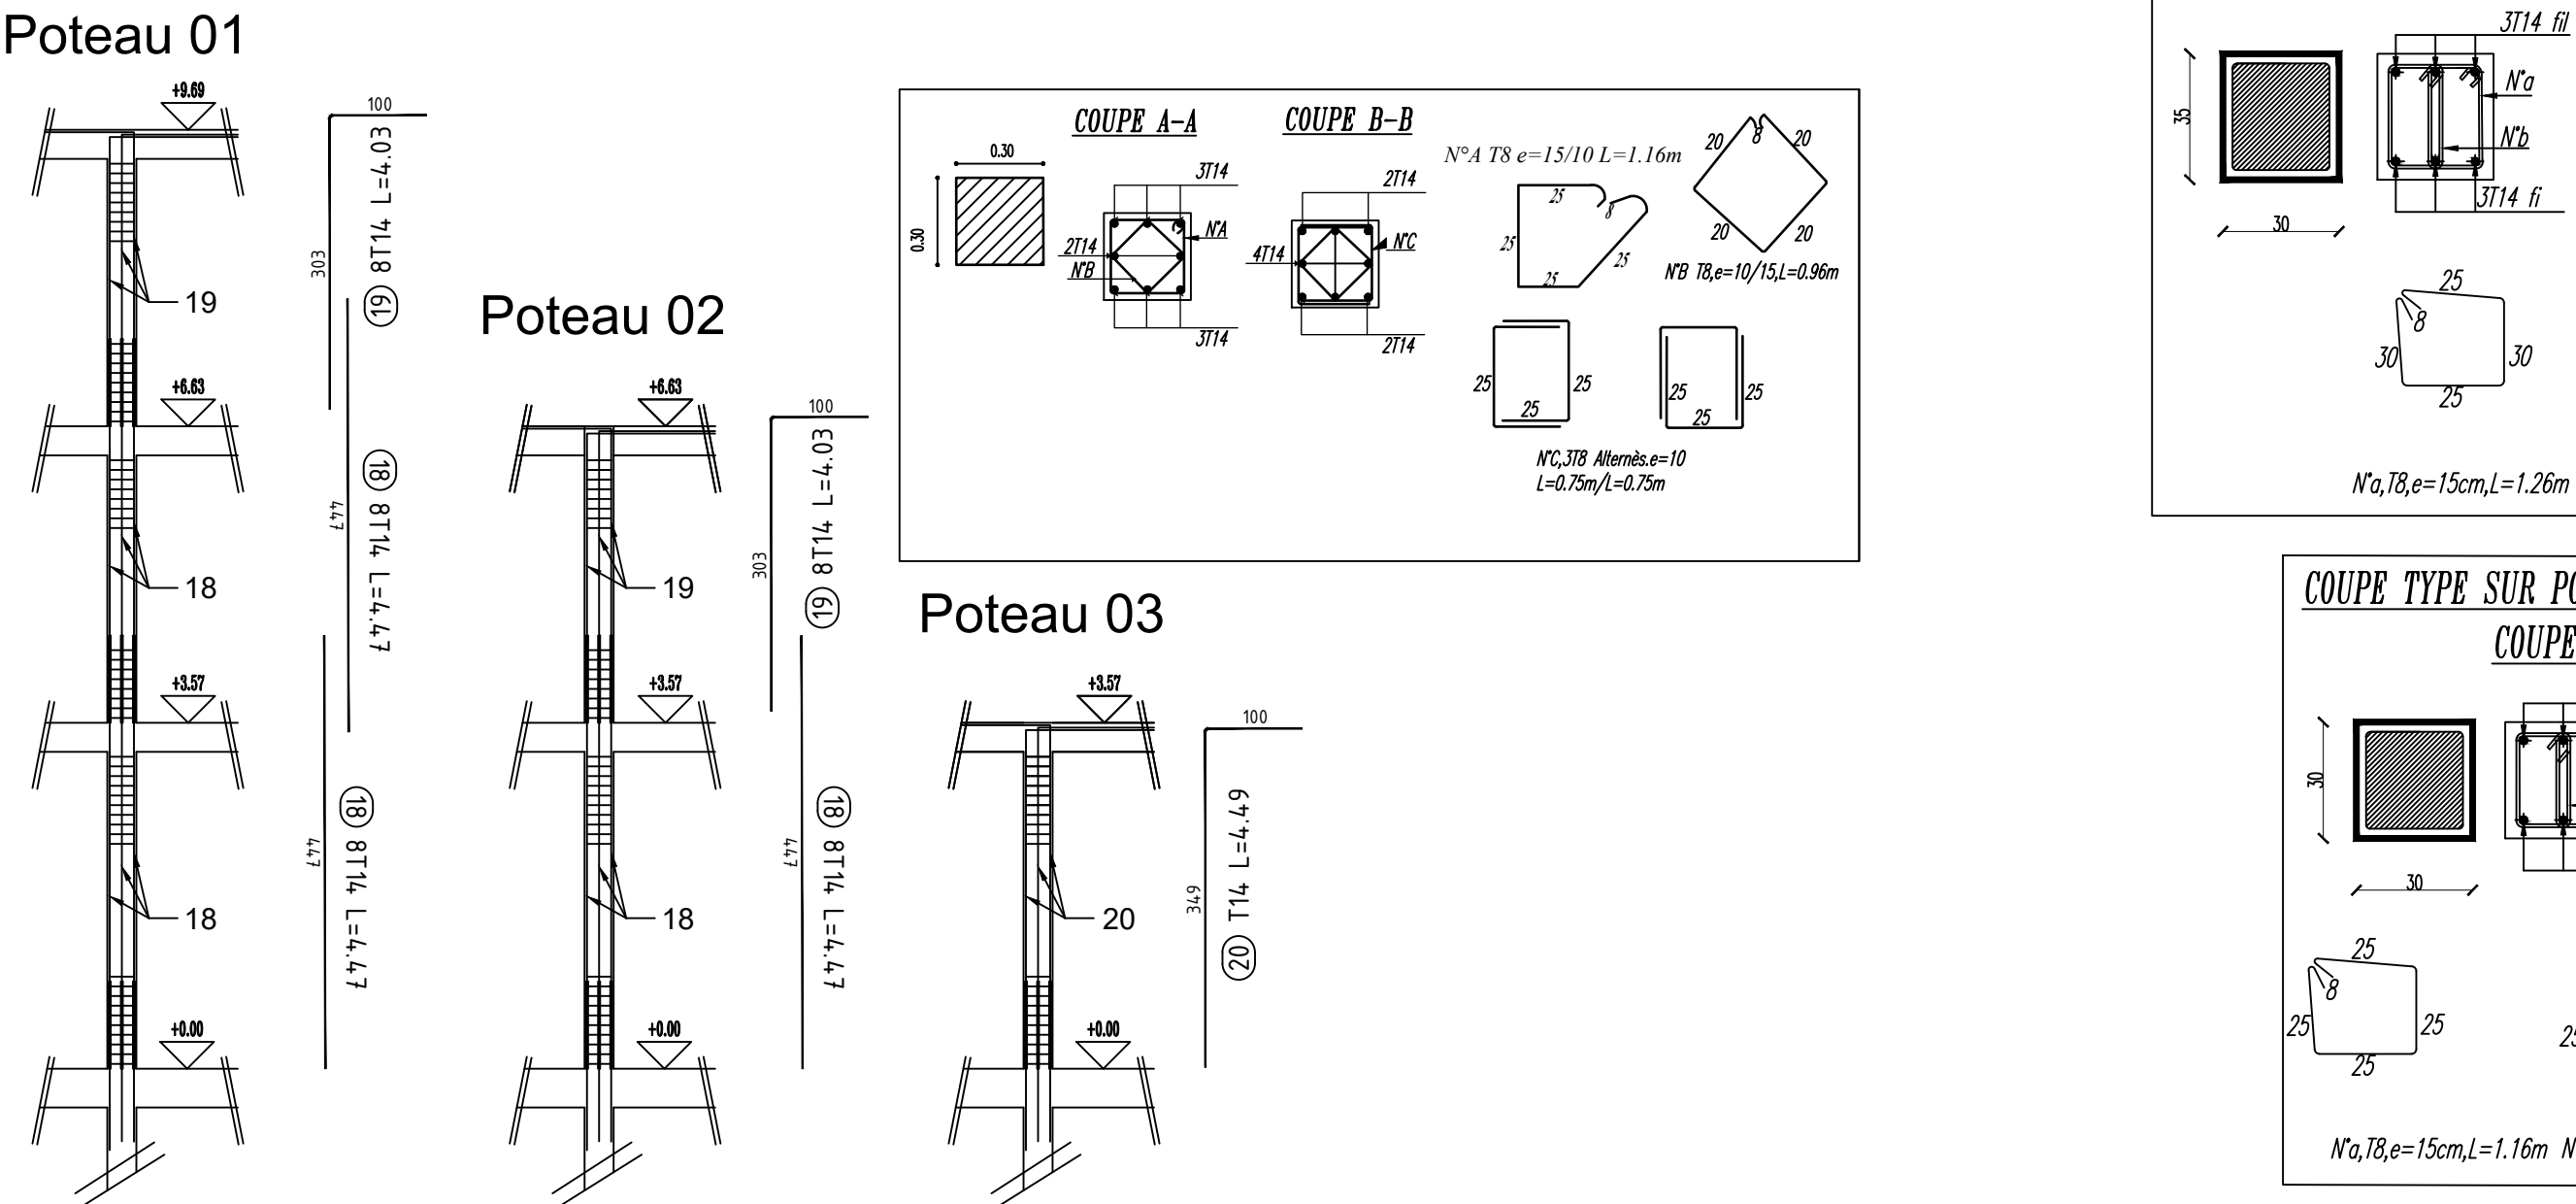

Coffrage Ferrailage Escalier

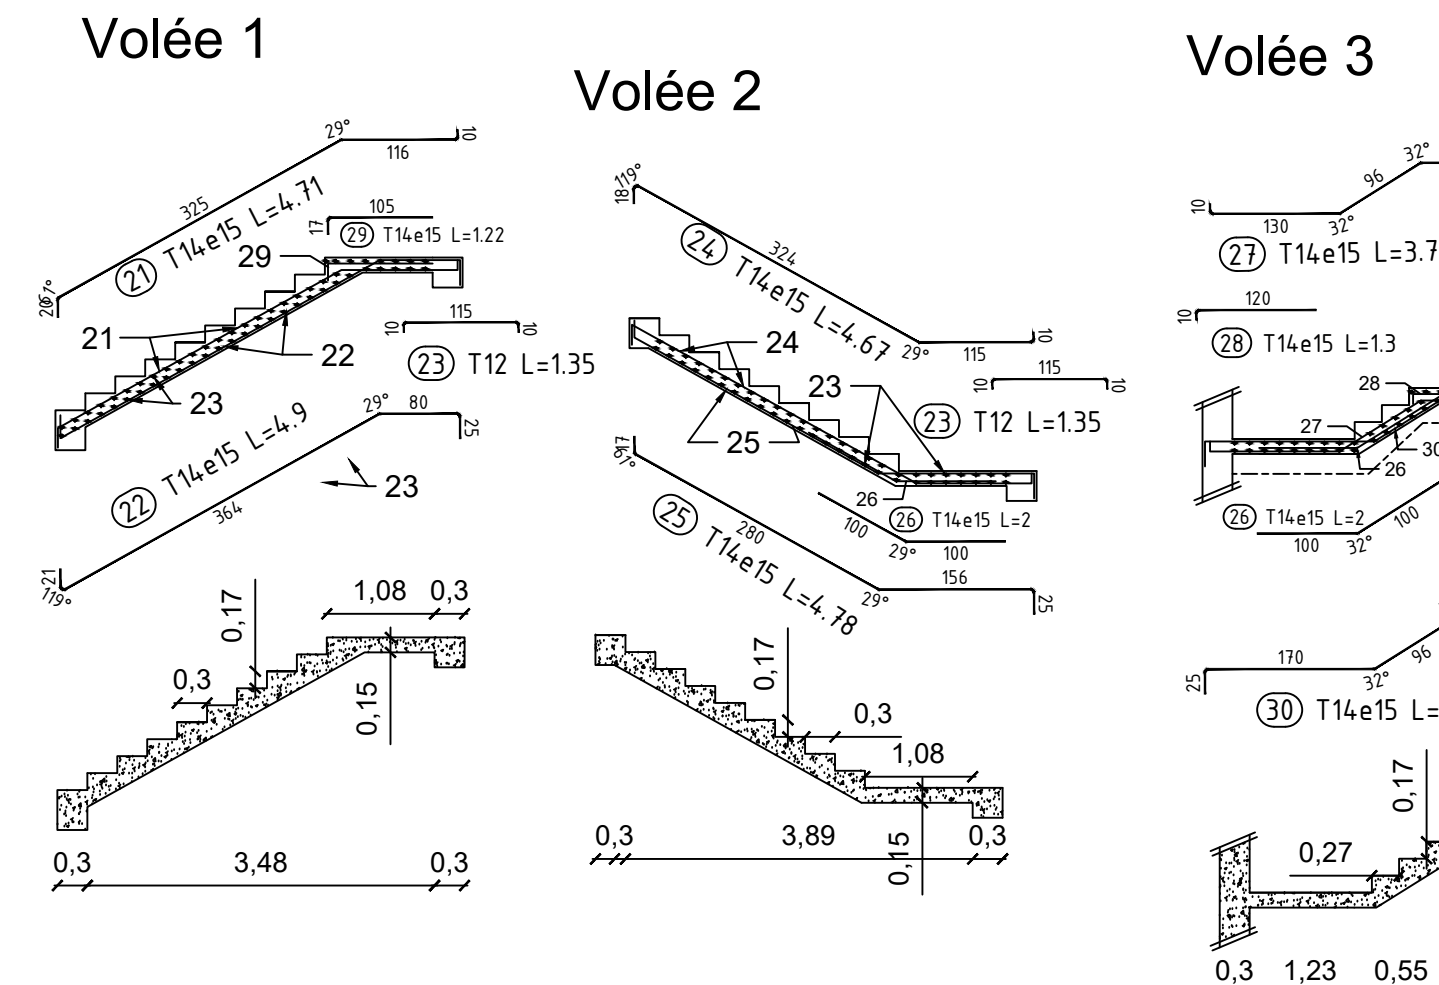

Bureau d'études technique de l'est
Z.A. CHIRANI SAGHBI N°58 EL KHROUB, CNE
0558 11 55 36 / 0698 97 02 25
bureautechniquelest@gmail.com

Projet : CONSTRUCTION A USAGE D'HABITATION
EN RDC + 2 ETAGES

Adresse : LOTISSEMENT BEN ABDELAMALEK RAMDHAN
LOT N° 57 CONSTANTINE

Maitre d'ouvrage : BOUBEKRI REDOUANE

PLAN :
COFFRAGE FERRAILAGE Fondation
COFFRAGE FERRAILAGE Niv RDC, +3.57, +6.63, +9.69
COFFRAGE FERRAILAGE Poteaux, Poutres, Escalier

Dessiné par : A.BOUARRROUDJ

N° de planche : 01

Echelle : 1/50
Echelle : 1/25

Obs / Réserves :

Scanné QR code

Code archive : BR-CNE-CNE-GC-026-11-25

date : 11/2025